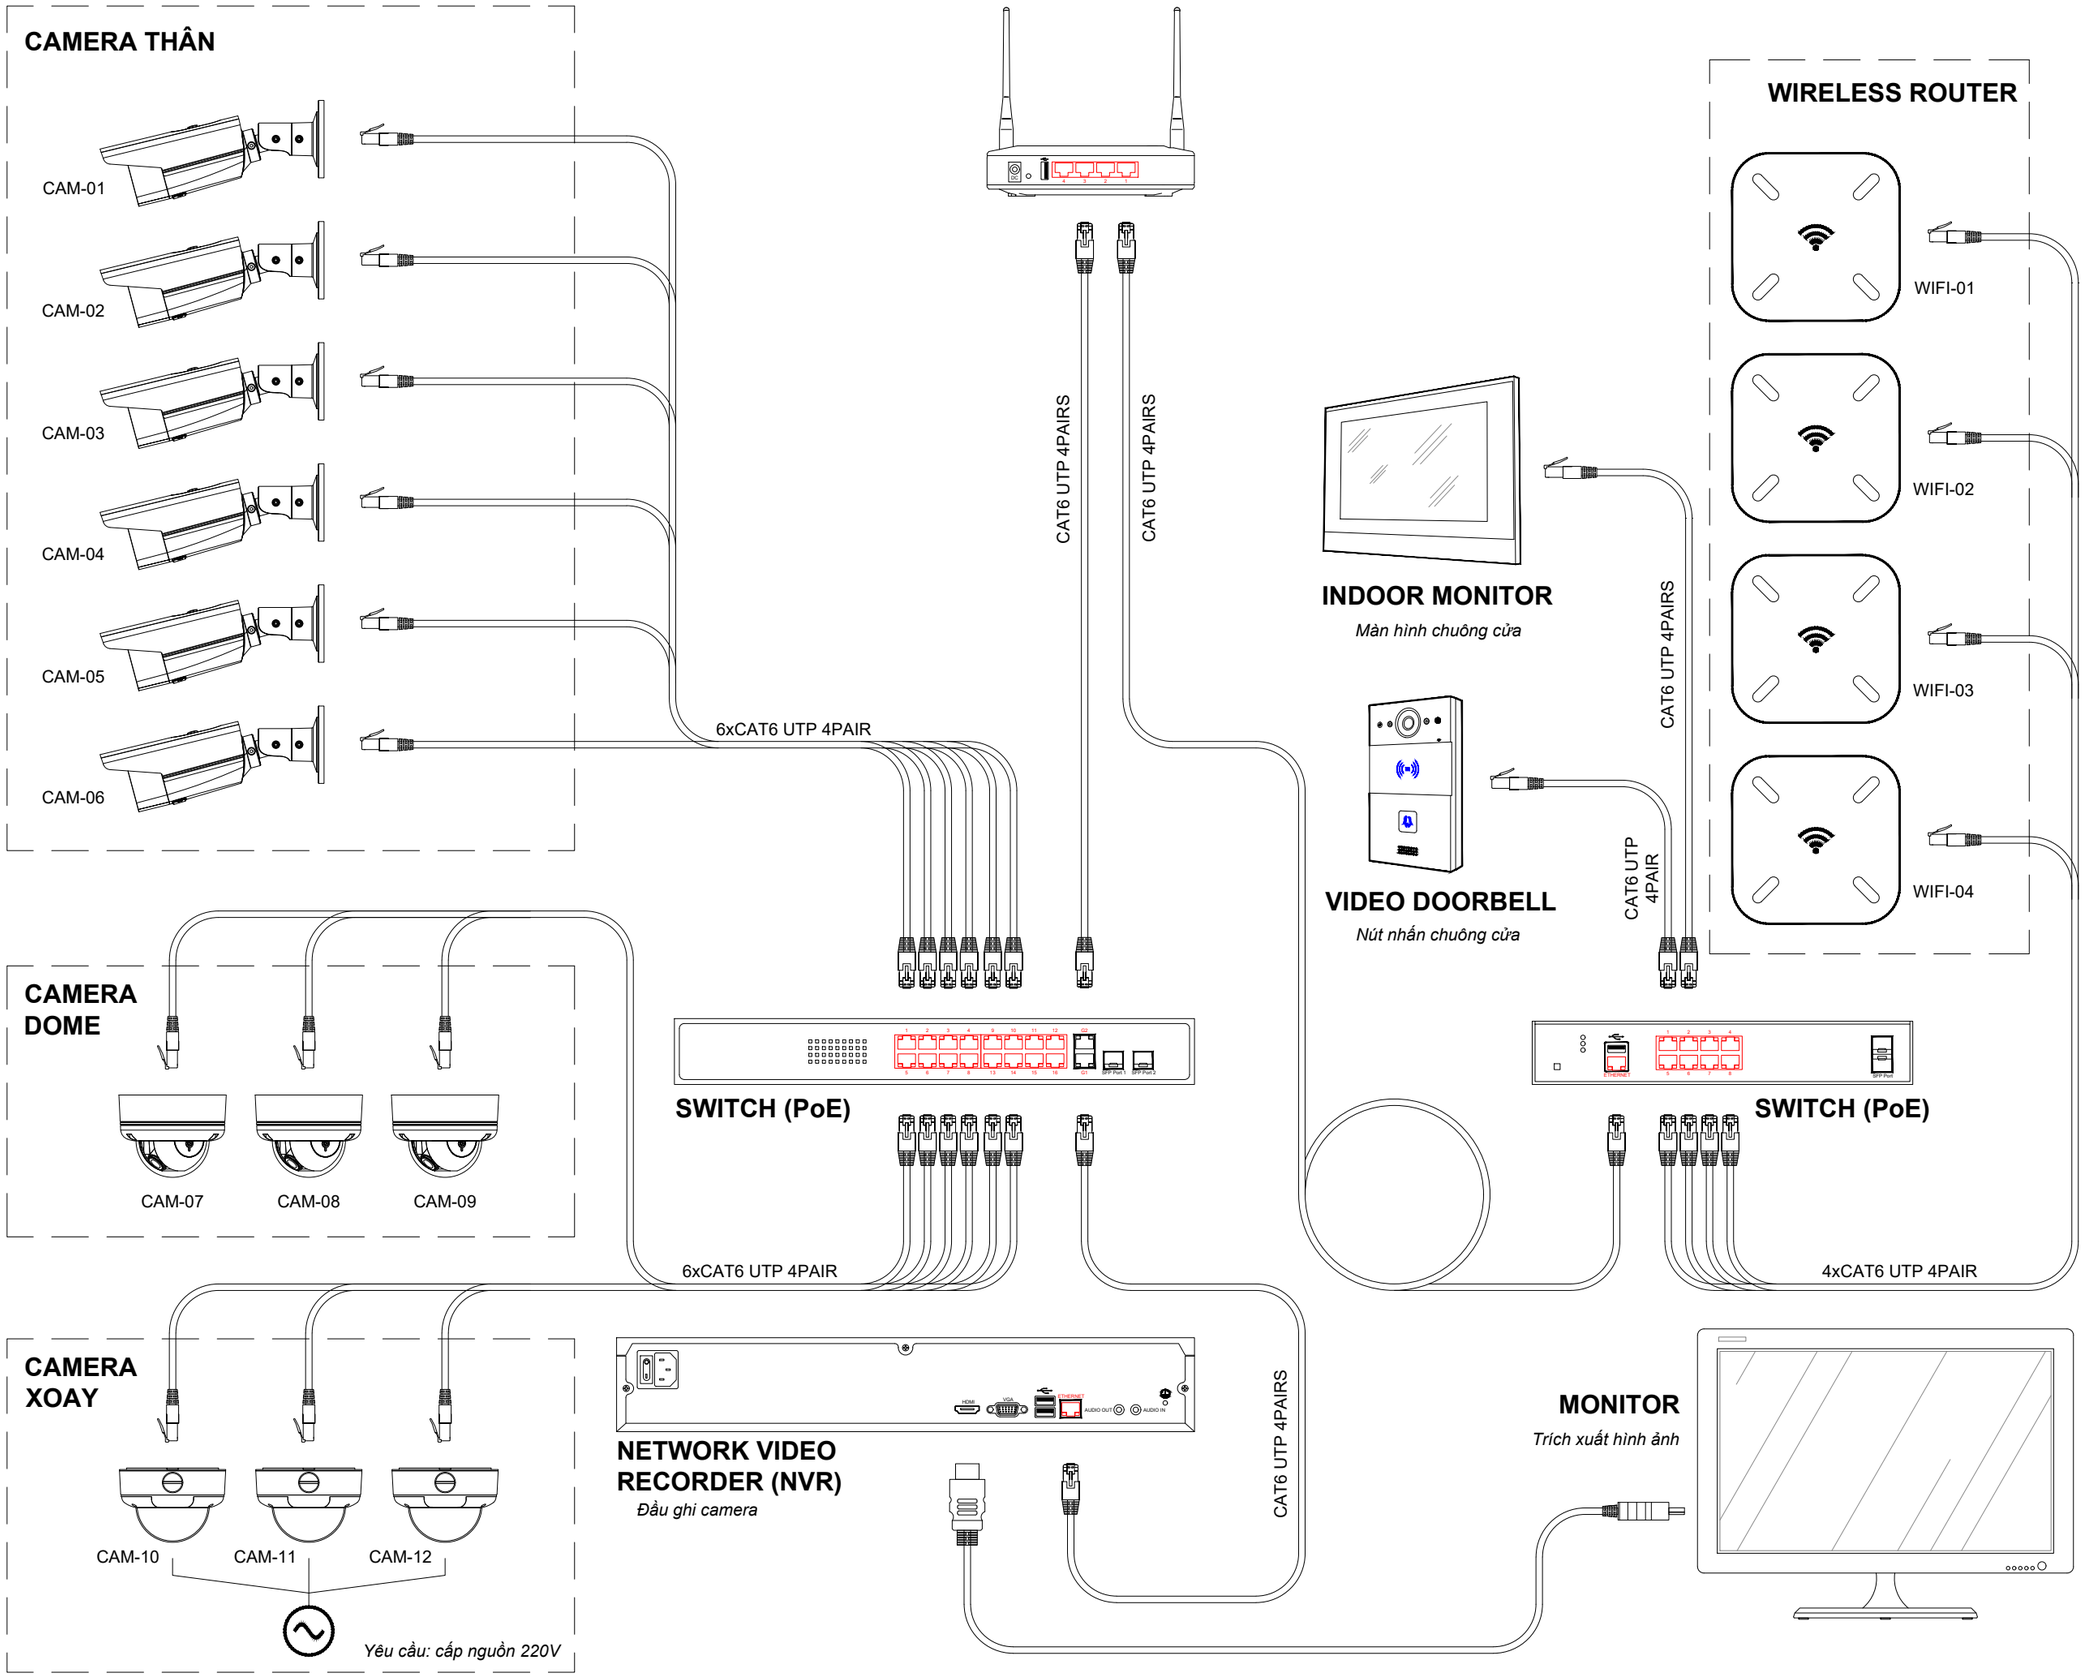

NGÀY HOÀN THÀNH	

HIỆU ĐÍNH

LẦN	NGÀY	THIẾT KẾ	DUYỆT

CHỦ ĐẦU TƯ

Địa chỉ: .....
.....

TÊN CÔNG TRÌNH

Địa điểm xây dựng:
.....
.....

CÔNG TY CỔ PHẦN CNTT-VIỄN THÔNG THẠCH ANH

thach anh
Simple - Smart - Secure

Địa chỉ: 121-123 Bạch Đằng, Phường 2, Quận Tân Bình, HCM
Website: https://thachanhitt.vn
Email: info@thachanhitt.vn
Tel: 091 888 2067 Hotline: 1900 29 99 68

TỔNG GIÁM ĐỐC

Nguyễn Hồng Thạnh

CHỦ TRÌ THIẾT KẾ

KS. Vũ Trọng Nhân Nghĩa

THIẾT KẾ

KS. Nguyễn Quang Nhật Trường

KIỂM TRA

KS. Vũ Trọng Nhân Nghĩa

TÊN BẢN VẼ

SƠ ĐỒ ĐI DÂY HỆ THỐNG CAMERA AN NINH VÀ WIFI ĐIỂN HÌNH

TỈ LỆ:	NL-03