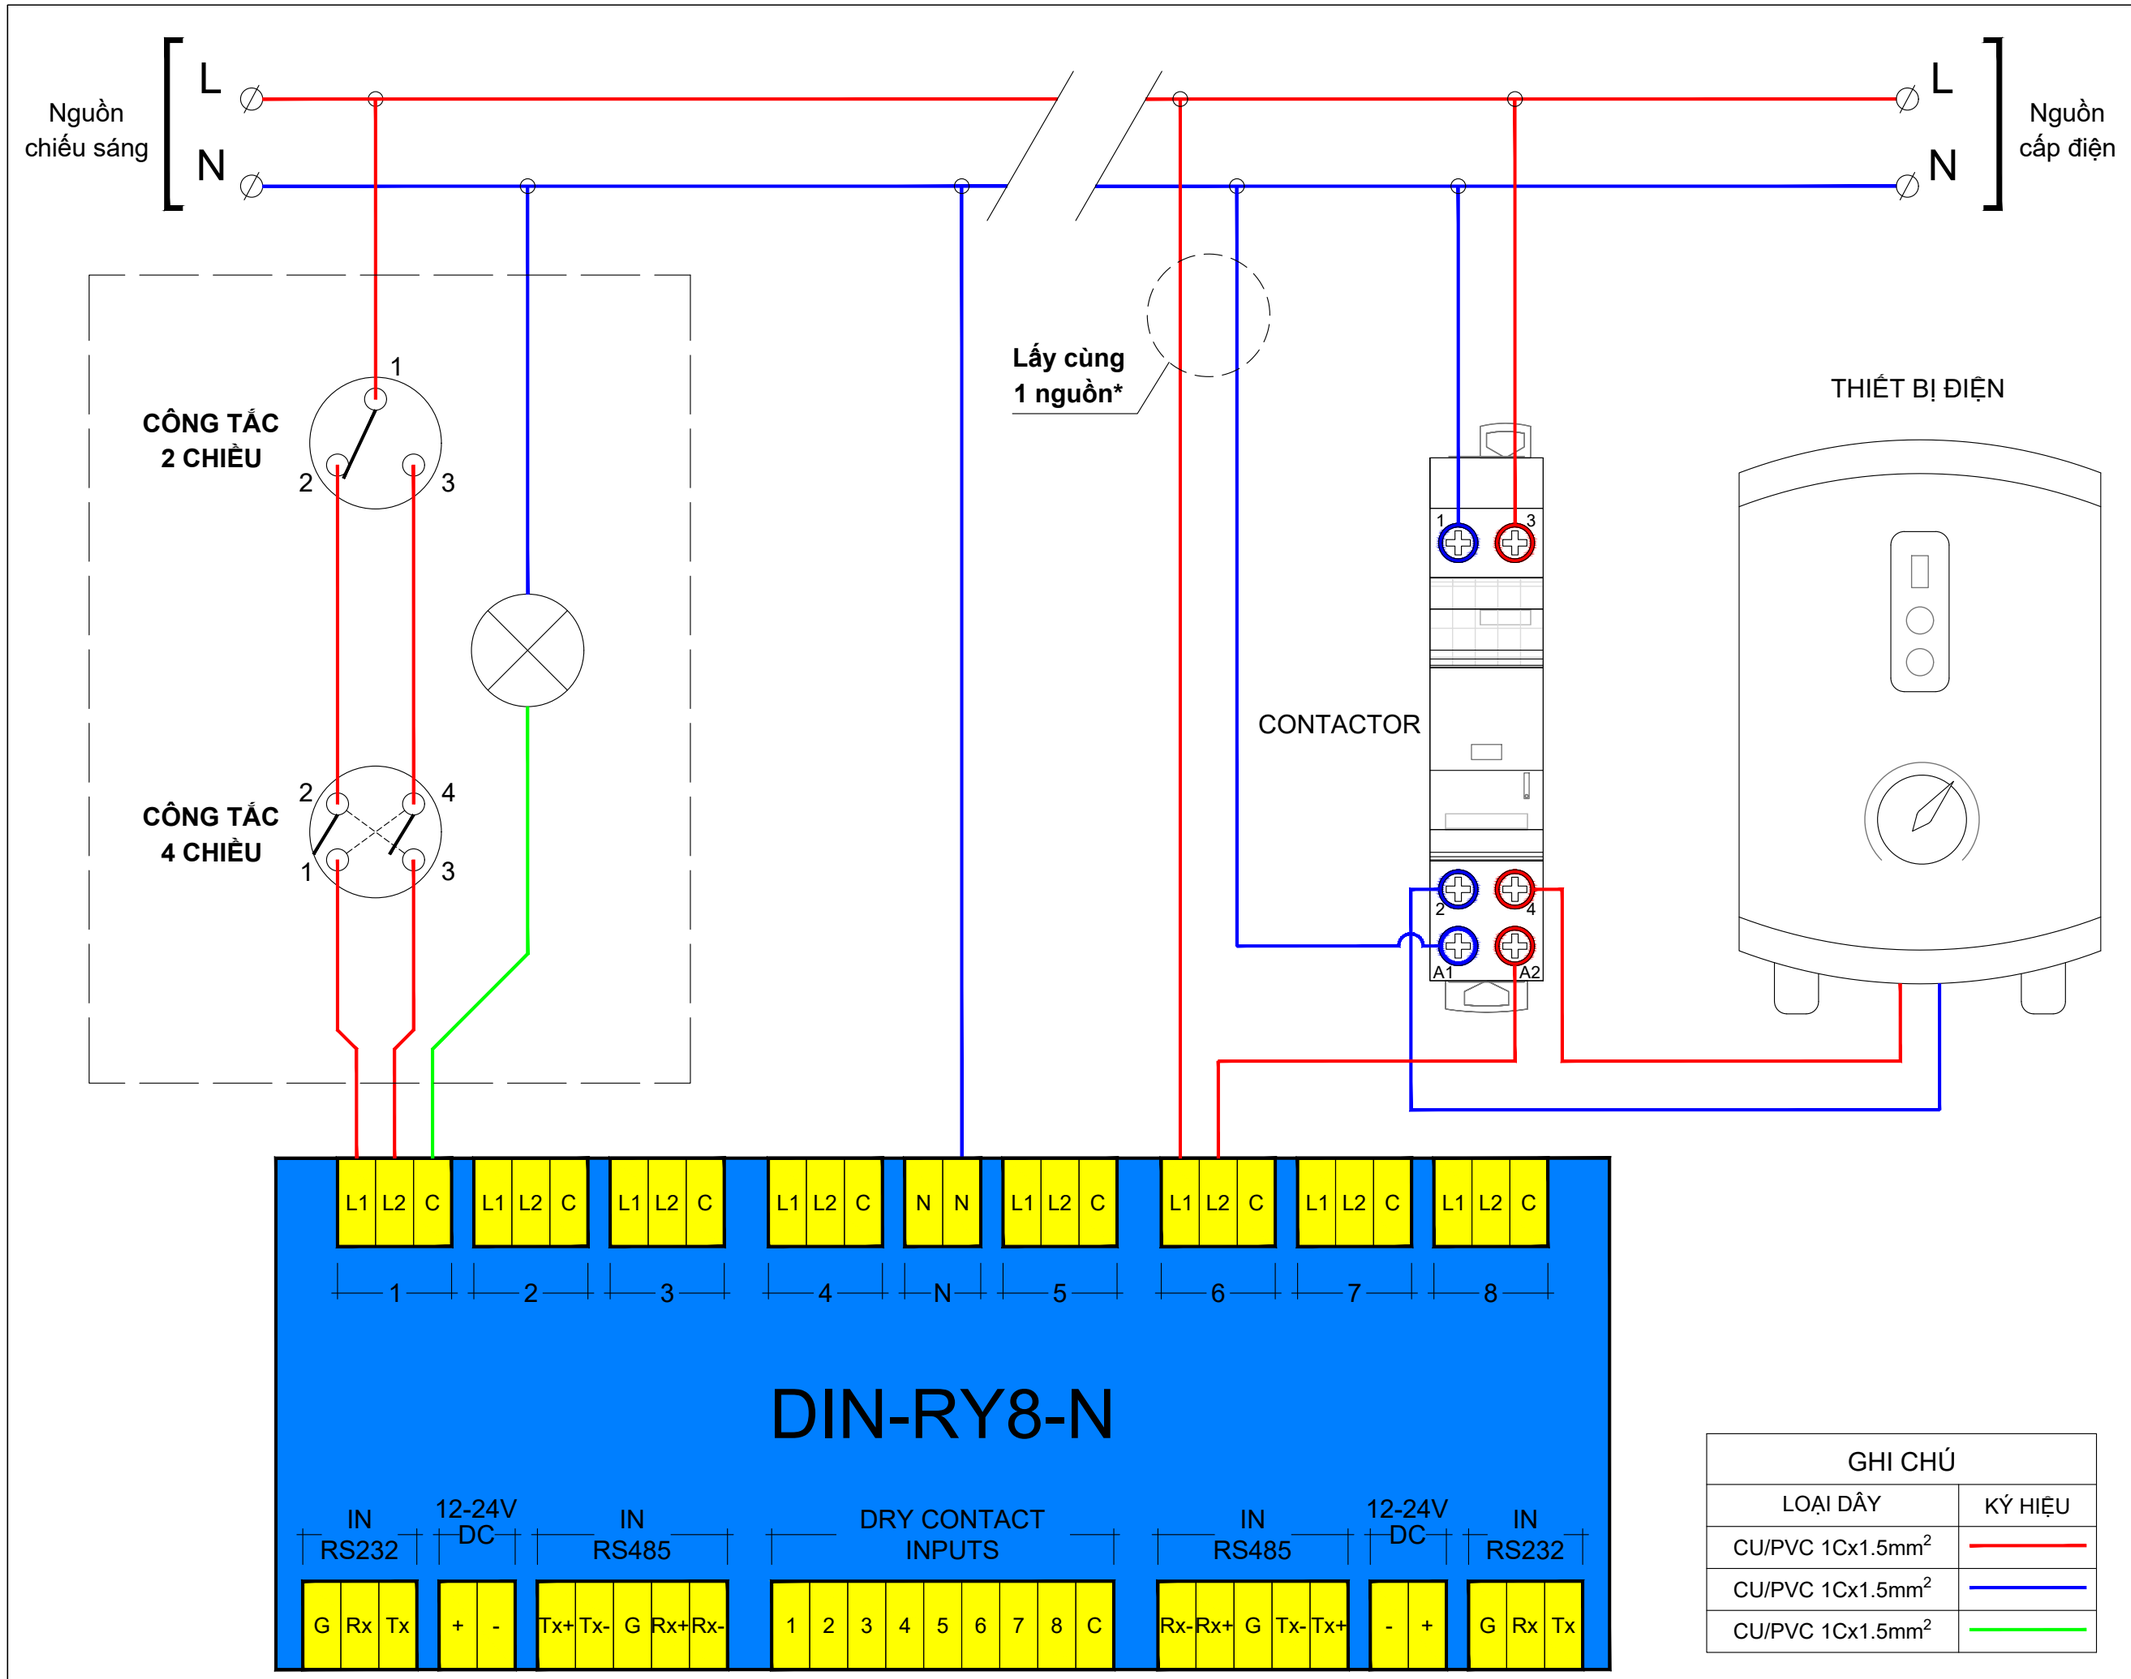

GHI CHÚ	
LOẠI DÂY	KÝ HIỆU
CU/PVC 1Cx1.5mm^2	
CU/PVC 1Cx1.5mm^2	
CU/PVC 1Cx1.5mm^2	

Ghi chú: *Lấy cùng một nguồn là lấy từ một vòng điện khép kín duy nhất. Ví dụ: không được lấy lửa (L) từ CB chiếu sáng và nguội (N) từ CB cấp điện.

NGÀY HOÀN THÀNH	

HIỆU ĐÍNH			
LẦN	NGÀY	THIẾT KẾ	DUYỆT

CHỦ ĐẦU TƯ

TÊN CÔNG TRÌNH

Địa điểm xây dựng:
.....
.....

CÔNG TY CỔ PHẦN CNTT-VIỄN THÔNG THẠNH ANH

thach anh
Simple - Smart - Secure

Địa chỉ: 121-123 Bạch Đằng, Phường 2, Quận Tân Bình, HCM
Website: https://thachanhitt.vn
Email: info@thachanhitt.vn
Tel: 091 888 2067 Hotline: 1900 29 99 68

TỔNG GIÁM ĐỐC
Nguyễn Hồng Thạch

CHỦ TRÌ THIẾT KẾ
Vũ Trọng Nhân Nghĩa

THIẾT KẾ
Nguyễn Quang Nhật Trường

KIỂM TRA
Vũ Trọng Nhân Nghĩa

TÊN BẢN VẼ
SƠ ĐỒ NGUYÊN LÝ ĐIỀU KHIỂN ĐÈN (CT 4 CHIỀU) VÀ THIẾT BỊ ĐIỆN

TỈ LỆ:	NL-05 (2)