CÁC THIẾT BỊ ĐIỀU KHIỂN

CÔNG TẮC ĐÈN (2 CHIỀU)

Yêu cầu:
- 2 dây nguồn 2 lõi **CADIVI VCmd 2x1.5 - 0,6/1kV từ công tắc về tủ thông minh.**

Lưu ý: Dây lửa vẫn thi công bình thường.

CÔNG TẮC KỊCH BẢN (ĐẢO ĐÈN)

Yêu cầu:
- 1 dây cáp mạng **CAT6 UTP 4PAIR kéo về tủ thông minh.**

MÀN HÌNH ĐIỀU KHIỂN MINI

Yêu cầu:
- 1 dây nguồn 2 lõi **CADIVI VCmd 2x1.5 - 0,6/1kV.**
- 1 dây cáp mạng **CAT6 UTP 4PAIR kéo về tủ thông minh.**

BỘ ĐIỀU KHIỂN HỒNG NGOẠI

Yêu cầu:
- 1 dây cáp mạng **CAT6 UTP 4PAIR kéo về tủ thông minh.**

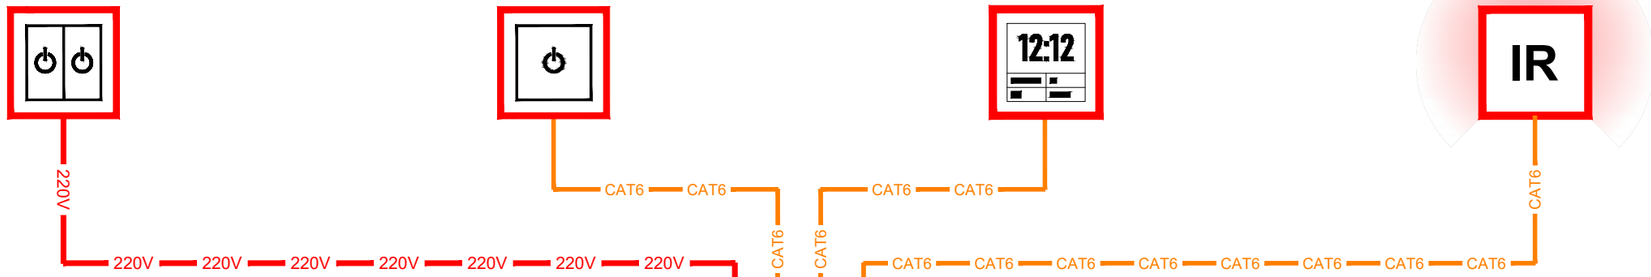

CÁC THIẾT BỊ CẢM BIẾN

CẢM BIẾN BÁO KHÓI

Yêu cầu:
- 1 dây cáp mạng **CAT6 UTP 4PAIR kéo về tủ thông minh.**

BEAM HÀNG RÀO

Yêu cầu:
- 1 dây cáp mạng **CAT6 UTP 4PAIR kéo về tủ thông minh.**

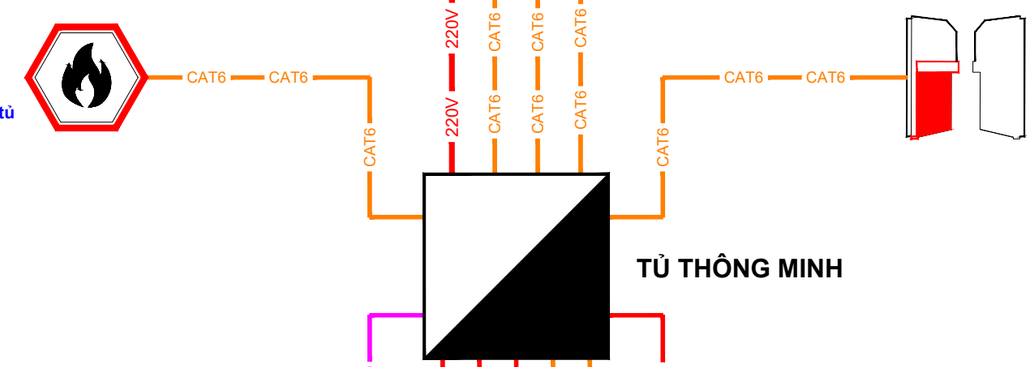

TỦ THÔNG MINH

CÔNG TẮC TỪ

Yêu cầu:
- 1 dây cáp điện thoại **SINO 2 đôi 4 lõi 1/0.5mmx2P kéo về tủ thông minh.**

CẢM BIẾN CHUYỂN ĐỘNG

Yêu cầu:
2 dây nguồn 2 lõi **CADIVI VCmd 2x1.5 - 0,6/1kV:**
- **1 dây cấp nguồn cho cảm biến,**
- **1 dây kéo từ cảm biến về tủ thông minh.**

CÁC THIẾT BỊ ĐƯỢC ĐIỀU KHIỂN

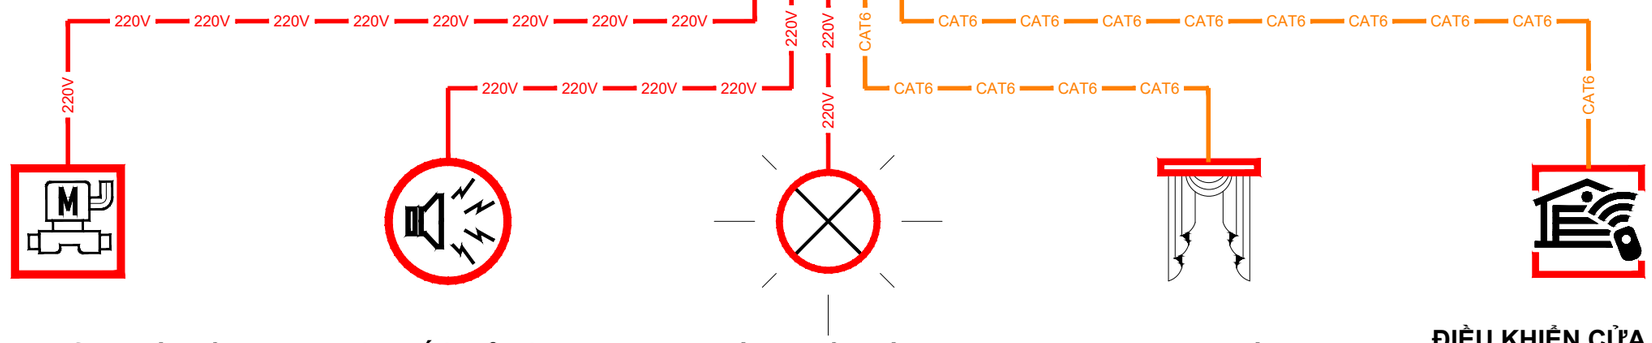

VAN ĐIỀU KHIỂN TƯỚI CÂY

Yêu cầu:
- 1 dây nguồn 2 lõi **CADIVI VCmd 2x1.5 - 0,6/1kV từ van về tủ thông minh.**
- **Nguồn chờ cấp nước.**

LOA BÁO ĐỘNG

Yêu cầu:
- 1 dây nguồn 2 lõi **CADIVI VCmd 1x1.5 - 0,6/1kV từ loa về tủ thông minh.**

ĐÈN CHIẾU SÁNG

Yêu cầu:
- 1 dây nguồn 1 lõi **CADIVI VCmd 1x1.5 - 0,6/1kV từ đèn về tủ thông minh.**

Lưu ý: Dây nguội vẫn thi công bình thường.

MOTOR RÈM

Yêu cầu:
- 1 dây nguồn 2 lõi **CADIVI VCmd 2x1.5 - 0,6/1kV.**
- 1 dây cáp mạng **CAT6 UTP 4PAIR kéo về tủ thông minh.**

ĐIỀU KHIỂN CỬA CỔNG / CỬA CUỐN

Yêu cầu:
- 1 dây nguồn 2 lõi **CADIVI VCmd 2x2.5 - 0,6/1kV.**
- 1 dây cáp mạng **CAT6 UTP 4PAIR kéo về tủ thông minh.**

NGÀY HOÀN THÀNH	

HIỆU ĐÍNH

LẦN	NGÀY	THIẾT KẾ	DUYỆT

CHỦ ĐẦU TƯ

Địa chỉ: .....
.....

TÊN CÔNG TRÌNH

Địa điểm xây dựng:
.....
.....

CÔNG TY CỔ PHẦN CNTT-VIỄN THÔNG THẠCH ANH

thach anh
Simple - Smart - Secure

Địa chỉ: 121-123 Bạch Đằng, Phường 2, Quận Tân Bình, HCM
Website: https://thachanhitt.vn
Email: info@thachanhitt.vn
Tel: 091 888 2067 Hotline: 1900 29 99 68

TỔNG GIÁM ĐỐC

Nguyễn Hồng Thạnh

CHỦ TRÌ THIẾT KẾ

KS. Vũ Trọng Nhân Nghĩa

THIẾT KẾ

KS. Nguyễn Quang Nhật Trường

KIỂM TRA

KS. Vũ Trọng Nhân Nghĩa

TÊN BẢN VẼ

SƠ ĐỒ NGUYÊN LÝ KẾT NỐI THIẾT BỊ VỀ TỦ THÔNG MINH

TỈ LỆ:	NL-02